


B

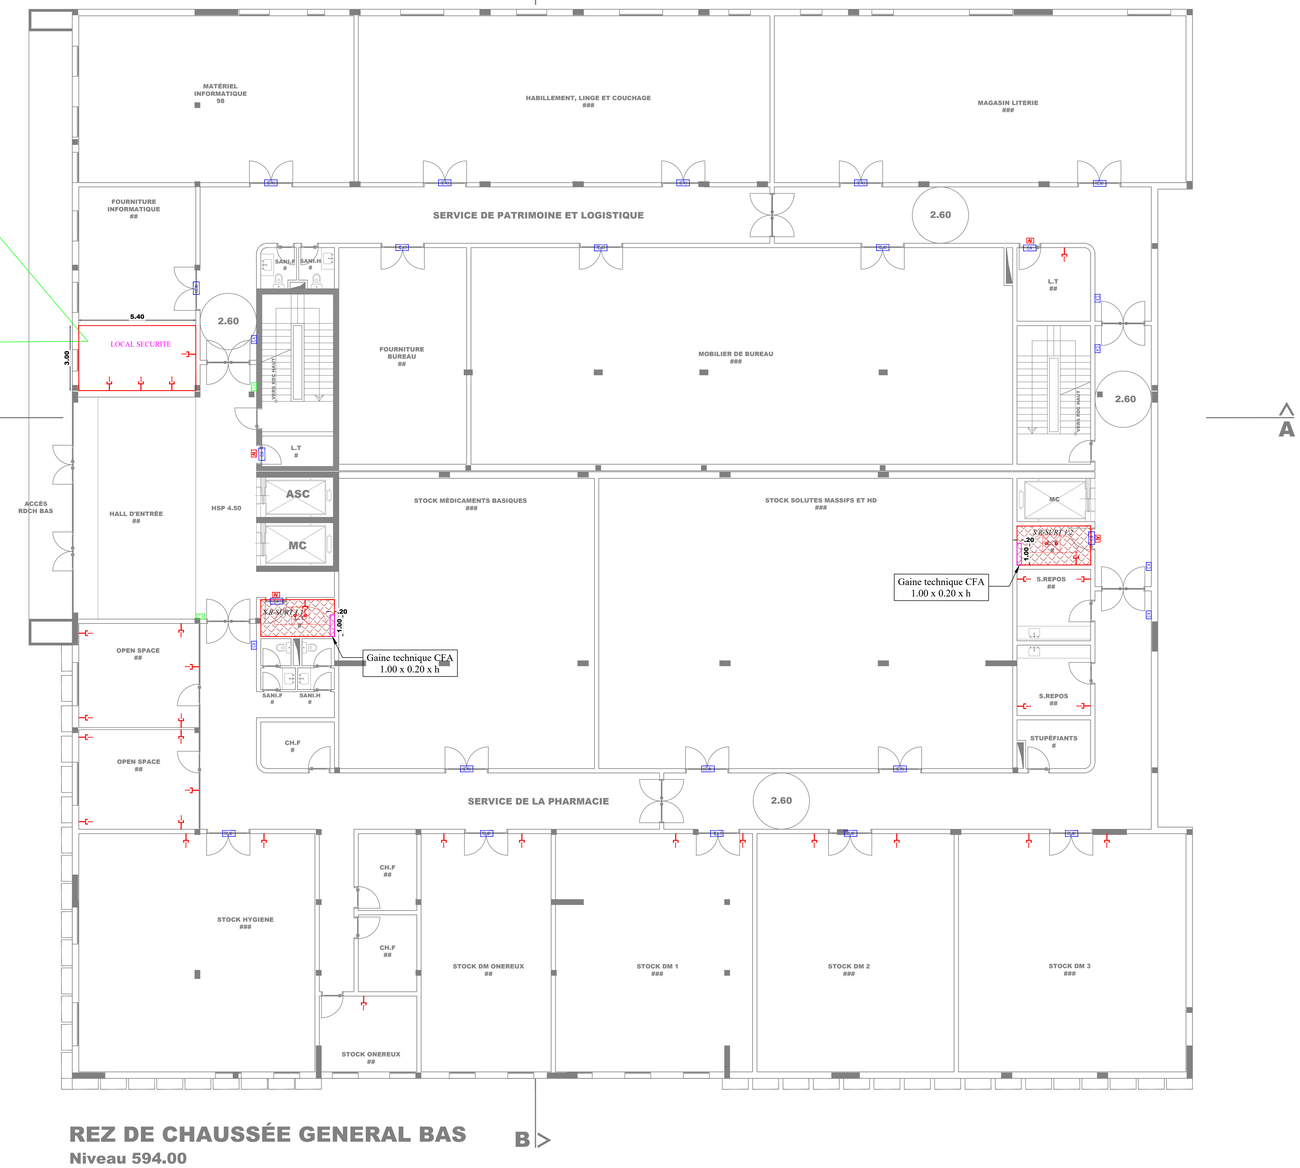

REZ DE CHAUSSÉE GENERAL BAS

Niveau 594.00

B

LEGENDE:

RESEAU VDI :

- SOUS REPARTITEUR INFORMATIQUE
- PRISE INFORMATIQUE
- ATTENTE POUR BORNE WIFI - CABLE RJ45 CAT6A S/FTP
- FAUX PLANCHER TECHNIQUE

CONTROLE D'ACCES, VIDEOSURVEILLANCE :

- POINT DE CONTROLE D'ACCES
- RESERVATION POUR CONTROLE D'ACCES
- ATTENTE POUR CAMÉRAS IP EXTÉRIEUR - CABLE RJ45 CAT6A S/FTP (HORS EQUIPEMENTS)
- ATTENTE POUR CAMÉRAS IP INTERIEUR - CABLE RJ45 CAT6A S/FTP (HORS EQUIPEMENTS)

AUDIO VIDEO :

- VIDEO PROJECTEUR Y COMPRIS SUPPORT DE FIXATION
- ECRAN DE PROJECTION MOTORISÉ
- BOITE AUDIO VIDEO
- PUPITRE DE CONFERENCE

N.B :

CÂBLE INFORMATIQUE DE TYPE CAT 6A 4P S/FTP EST PRÉVU POUR LES PRISES RJ45, ATTENTES POUR BORNES WIFI, ATTENTES POUR CAMÉRAS DE VIDÉO SURVEILLANCE, ATTENTES POUR CONTRÔLE D'ACCES

ROYAUME DU MAROC
WILAYA DE LA RÉGION DE L'ORIENTAL
PROVINCE DE OUJDA
COMMUNE OUJDA

MAITRE D'OUVRAGE

ROYAUME DU MAROC
MINISTERE DE LA SANTÉ ET DE LAPROTECTION SOCOIALE
CENTRE HOSPITALIER UNIVERSITAIRE MOHAMMED VI OUJDA

PROJET:
PROJET DE CONSTRUCTION D'UNE PLATEFORME LOGISTIQUE AU CENTRE HOSPITALO-UNIVERSITAIRE MOHAMMED VI OUJDA

SIS A : | TITRE FONCIER N°: -

DOCUMENTS D'ENTREE:

BATIMENTS	DESIGNATION	CORPS D'ETAT
PLATEFORME LOGISTIQUE - CHU OUJDA	PLAN D'IMPLANTATION EQUIPEMENTS COURANT FAIBLE - RDC BAS	ELECTRICITE COURANT FAIBLE

CODE PROJET	PHASE ETUDES	CODE PLAN	ZONE	N° PLAN	IND	DATE
421	PE	ECF	--	05	-	

ECHELLE 1/100

ARCHITECTE

HASSAN ALLA
alla.architecte@gmail.com

BUREAU D'ETUDES TECHNIQUES

OMNIUM TECHNOLOGIQUE
ASSISTANCE & ETUDE
Avenue Addolia, Hay Riyad - Rabat
Tél : +212 5 37 57 28 28
Fax: +212 5 37 57 10 77
contact@omtec.com

BUREAU DE CONTRÔLE

DEKRA Inspection SA
DEKRA Inspection SA
Bureau de Prévention et de Contrôle Technique

Ce document est la propriété d'OMNIUM TECHNOLOGIQUE et ne peut être reproduit ou communiqué sans son autorisation

IND.	Projeté	Etudié	Vérifié	Motif d'indice et/ou historique	Date	Etat
-				Emission initiale		
A						
B						
C						
D						
E						