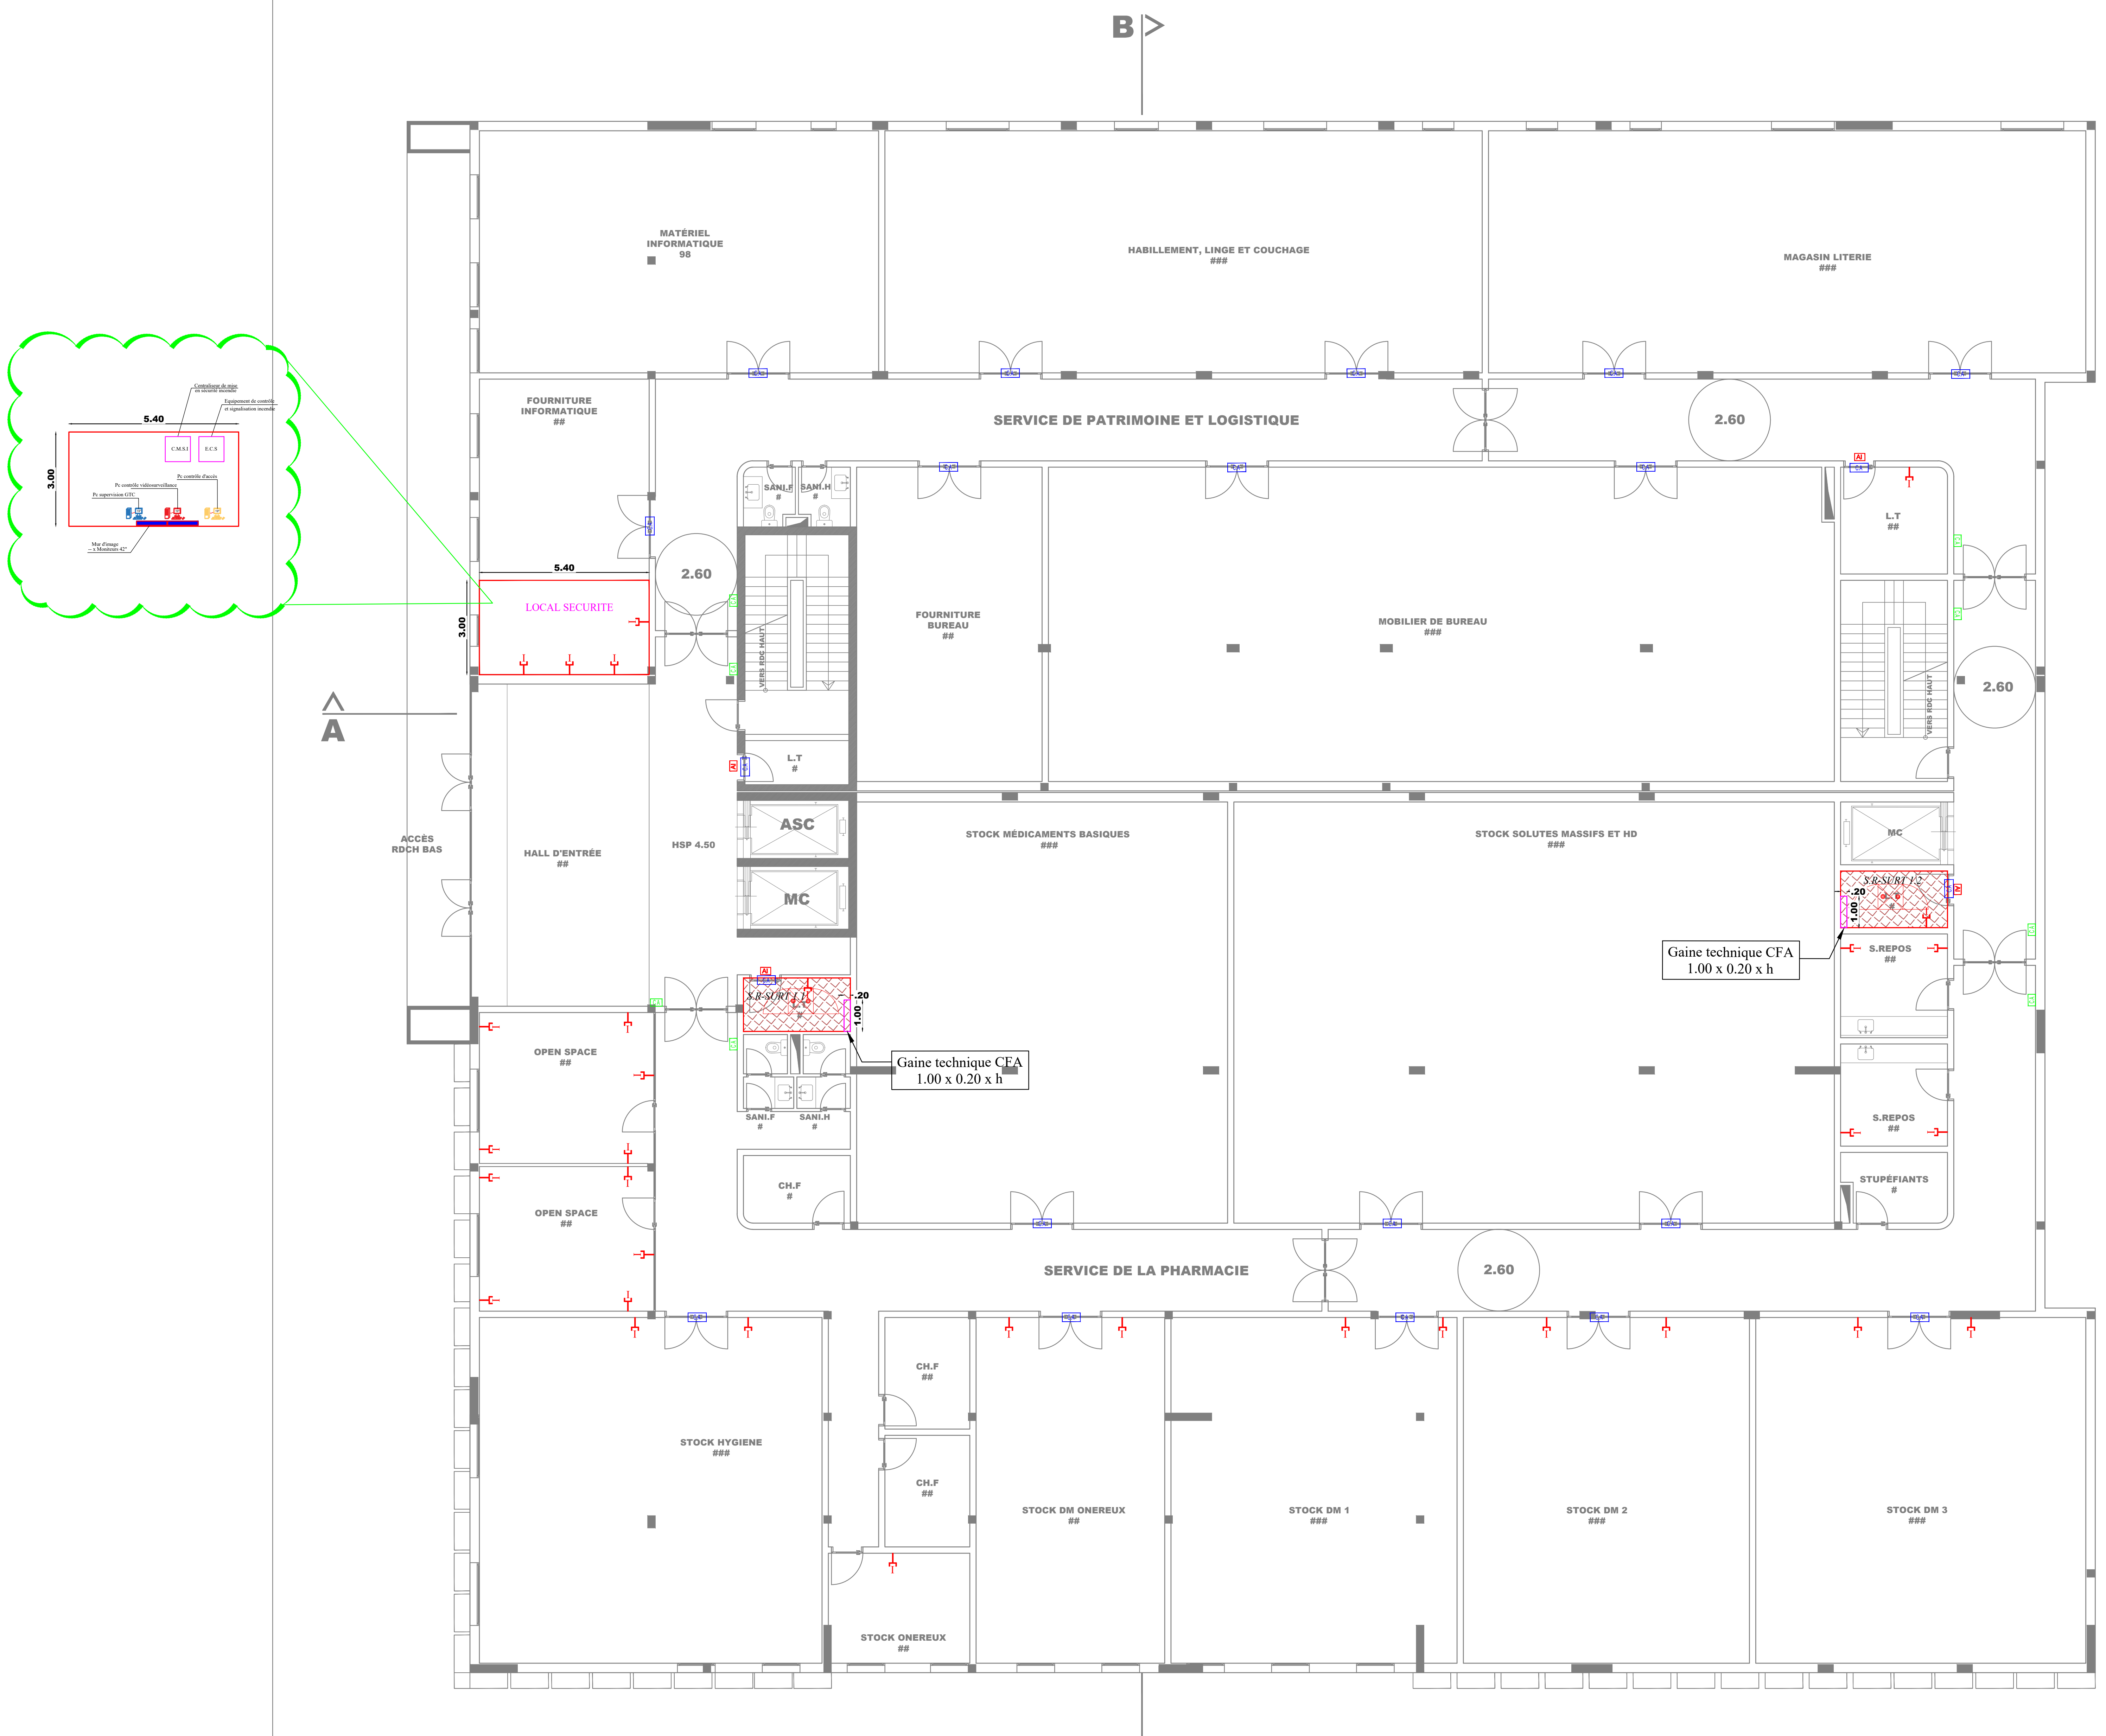
B
MATÉRIEL INFORMATIQUE
98
HABILLEMENT, LINGE ET COUCHAGE
###
MAGASIN LITERIE
###
FOURNITURE INFORMATIQUE
##
SERVICE DE PATRIMOINE ET LOGISTIQUE
2.60
5.40
3.00
LOCAL SECURITE
SANI.F
SANI.H
FOURNITURE BUREAU
##
MOBILIER DE BUREAU
###
L.T
A
ACCÈS RDCH BAS
HALL D'ENTRÉE
HSP 4.50
ASC
MC
STOCK MÉDICAMENTS BASIQUES
###
STOCK SOLUTES MASSIFS ET HD
###
S.REPOS
Gaine technique CFA
1.00 x 0.20 x h
OPEN SPACE
CH.F
STUPÉFIANTS
SERVICE DE LA PHARMACIE
STOCK HYGIENE
STOCK DM ONEREUX
STOCK DM 1
STOCK DM 2
STOCK DM 3
STOCK ONEREUX

REZ DE CHAUSSÉE GENERAL BAS

Niveau 594.00

LEGENDE:

RESEAU VDI :

SOUS REPARTITEUR INFORMATIQUE

PRISE INFORMATIQUE

ATTENTE POUR BORNE WIFI - CABLE RJ45 CAT6A S/FTP

Faux plancher — FAUX PLANCHER TECHNIQUE

CONTROLE D'ACCES, VIDEOSURVEILLANCE :

CA — POINT DE CONTROLE D'ACCES

CA — RESERVATION POUR CONTROLE D'ACCES

ATTENTE POUR CAMÉRAS IP EXTÉRIEUR - CABLE RJ45 CAT6A S/FTP (HORS EQUIPEMENTS)

ATTENTE POUR CAMÉRAS IP INTERIEUR - CABLE RJ45 CAT6A S/FTP (HORS EQUIPEMENTS)

AUDIO VIDEO :

VIDEO PROJECTEUR Y COMPRIS SUPPORT DE FIXATION

ECRAN DE PROJECTION MOTORISÉ

AV — BOITE AUDIO VIDEO

PUPITRE DE CONFERENCE

N.B :

CÂBLE INFORMATIQUE DE TYPE CAT 6A 4P S/FTP EST PRÉVU POUR LES PRISES RJ45, ATTENTES POUR BORNES WIFI, ATTENTES POUR CAMÉRAS DE VIDÉO SURVEILLANCE, ATTENTES POUR CONTRÔLE D'ACCES

ROYAUME DU MAROC
WILAYA DE LA RÉGION DE L'ORIENTAL
PROVINCE DE OUJDA
COMMUNE OUJDA

MAITRE D'OUVRAGE

ROYAUME DU MAROC
MINISTERE DE LA SANTÉ ET DE LAPROTECTION SOCOIALE
CENTRE HOSPITALIER UNIVERSITAIRE MOHAMMED VI OUJDA

PROJET:
PROJET DE CONSTRUCTION D'UNE PLATEFORME LOGISTIQUE AU CENTRE HOSPITALO-UNIVERSITAIRE MOHAMMED VI OUJDA

SIS A :		TITRE FONCIER N°:	-

DOCUMENTS D'ENTREE:

BATIMENTS	DESIGNATION	CORPS D'ETAT
PLATEFORME LOGISTIQUE - CHU OUJDA	PLAN D'IMPLANTATION EQUIPEMENTS COURANT FAIBLE - RDC BAS	ELECTRICITE COURANT FAIBLE

CODE PROJET	PHASE ETUDES	CODE PLAN	ZONE	N° PLAN	IND	DATE
4 2 1	P E	E C F	- -	0 5	-	ECHELLE 1/100

ARCHITECTE

HASSAN ALLA
alla.architecte@gmail.com

BUREAU D'ETUDES TECHNIQUES	BUREAU DE CONTRÔLE
OMNIUM TECHNOLOGIQUE ASSISTANCE & ETUDE 5,Avenue Addolb, Hay Riyad - Rabat Tel: +2125 37 57 28 28 Fax: +212 5 37 57 10 77 contact@omteq.com	DEKRA Inspection SA Bureau de Prévention et de Contrôle Technique DEKRA Inspection SA

Ce document est la propriété d'OMNIUM TECHNOLOGIQUE et ne peut être reproduit ou communiqué sans son autorisation

IND.	Projeté	Etudié	Vérifié	Motif d'indice et/ou historique	Date	Etat
				Emission initiale		
A						
B						
C						
D						
E						