
PLAN: RDC BAS


NODES
RB-A: CFA riser A - PoE switch + UPS
RB-B: CFA riser nearest LOCAL SECURITE - PoE switch + UPS
CR: LOCAL SECURITE - VMS + 4 displays + access switch

CABLING
Control room selected: LOCAL SECURITE
RB-A and RB-B receive OS2 10G uplinks to MDF on ETAGE
Cat6A RB-B to control switch - verify permanent link <= 90 m

Legend: magenta = fibre; green = Cat6A
CONCEPT ONLY - routes require site survey

CCTV NETWORK ARCHITECTURE - CONCEPT

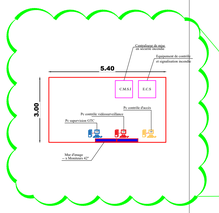

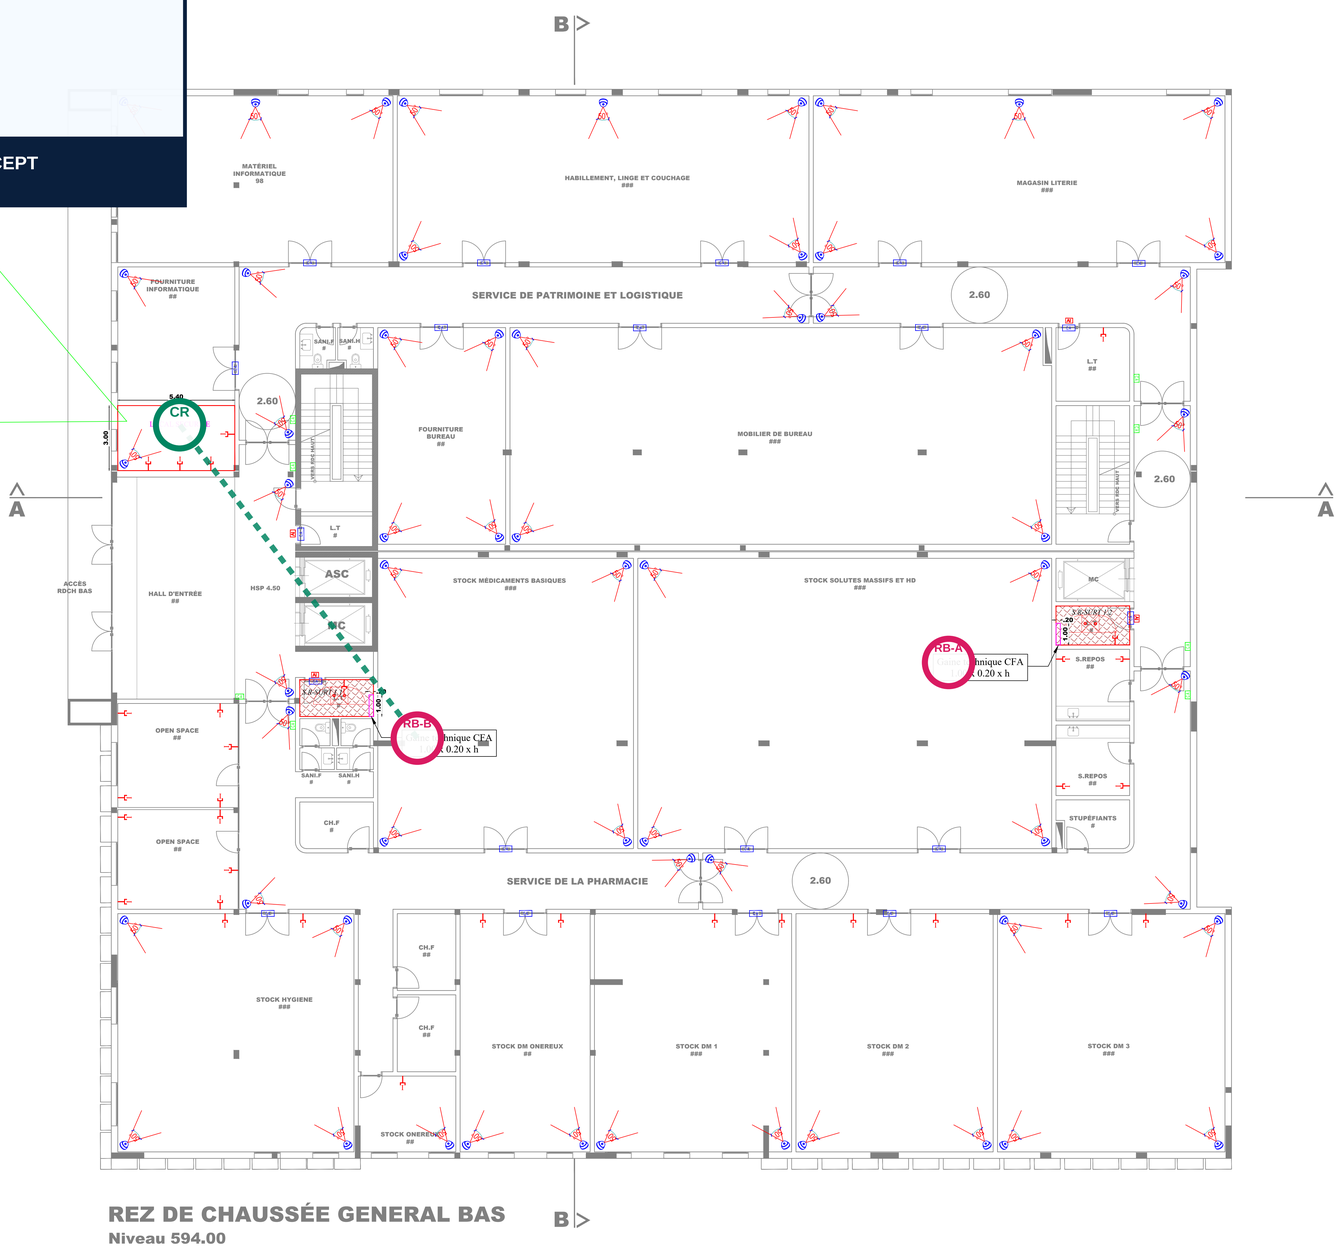

LEGENDE:

RESEAU VDI :

- SOUS REPARTITEUR INFORMATIQUE
- PRISE INFORMATIQUE
- ATTENTE POUR BORNE WIFI - CABLE RJ45 CAT6A S/FTP
- FAUX PLANCHER TECHNIQUE

CONTROLE D'ACCES, VIDEOSURVEILLANCE :

- POINT DE CONTROLE D'ACCES
- RESERVATION POUR CONTROLE D'ACCES
- ATTENTE POUR CAMÉRAS IP EXTÉRIEUR - CABLE RJ45 CAT6A S/FTP (HORS EQUIPEMENTS)
- ATTENTE POUR CAMÉRAS IP INTERIEUR - CABLE RJ45 CAT6A S/FTP (HORS EQUIPEMENTS)

AUDIO VIDEO :

- VIDEO PROJECTEUR Y COMPRIS SUPPORT DE FIXATION
- ECRAN DE PROJECTION MOTORISÉ
- BOITE AUDIO VIDEO
- PUPITRE DE CONFERENCE

N.B :

CÂBLE INFORMATIQUE DE TYPE CAT 6A 4P S/FTP EST PRÉVU POUR LES PRISES RJ45, ATTENTES POUR BORNES WIFI, ATTENTES POUR CAMÉRAS DE VIDÉO SURVEILLANCE, ATTENTES POUR CONTRÔLE D'ACCES

ROYAUME DU MAROC
WILAYA DE LA RÉGION DE L'ORIENTAL
PROVINCE DE OUJDA
COMMUNE OUJDA

MAITRE D'OUVRAGE

ROYAUME DU MAROC
MINISTERE DE LA SANTÉ ET DE LAPROTECTION SOCOIALE
CENTRE HOSPITALIER UNIVERSITAIRE MOHAMMED VI OUJDA

PROJET:
PROJET DE CONSTRUCTION D'UNE PLATEFORME LOGISTIQUE AU CENTRE HOSPITALO-UNIVERSITAIRE MOHAMMED VI OUJDA

SIS A : | TITRE FONCIER N°: -

DOCUMENTS D'ENTREE:

BATIMENTS	DESIGNATION	CORPS D'ETAT
PLATEFORME LOGISTIQUE - CHU OUJDA	PLAN D'IMPLANTATION EQUIPEMENTS COURANT FAIBLE - RDC BAS	ELECTRICITE COURANT FAIBLE

CODE PROJET	PHASE ETUDES	CODE PLAN	ZONE	N° PLAN	IND	DATE
421	PE	ECF	- -	05	-	

ECHELLE 1/100

ARCHITECTE
HASSAN ALLA
alla.architecte@gmail.com

BUREAU D'ETUDES TECHNIQUES: OMNIUM TECHNOLOGIQUE
OMNIUM TECHNOLOGIQUE
ASSISTANCE & ETUDE
Avenue Addiba, Hay Riyad - Rabat
Tél : +212 5 37 57 28 28
Fax: +212 5 37 57 10 77
contact@omtec.com

BUREAU DE CONTRÔLE: DEKRA
DEKRA Inspection SA
DEKRA Inspection SA
Bureau de Prévention et de Contrôle Technique

Ce document est la propriété d'OMNIUM TECHNOLOGIQUE et ne peut être reproduit ou communiqué sans son autorisation

IND.	Projeté	Etudié	Vérifié	Motif d'indice et/ou historique	Date	Etat
-				Emission initiale		
A						
B						
C						
D						
E						