
Schéma général de raccordement

Les liaisons cuivre et fibre optique déjà établies sont utilisées par l'ensemble de l'installation.

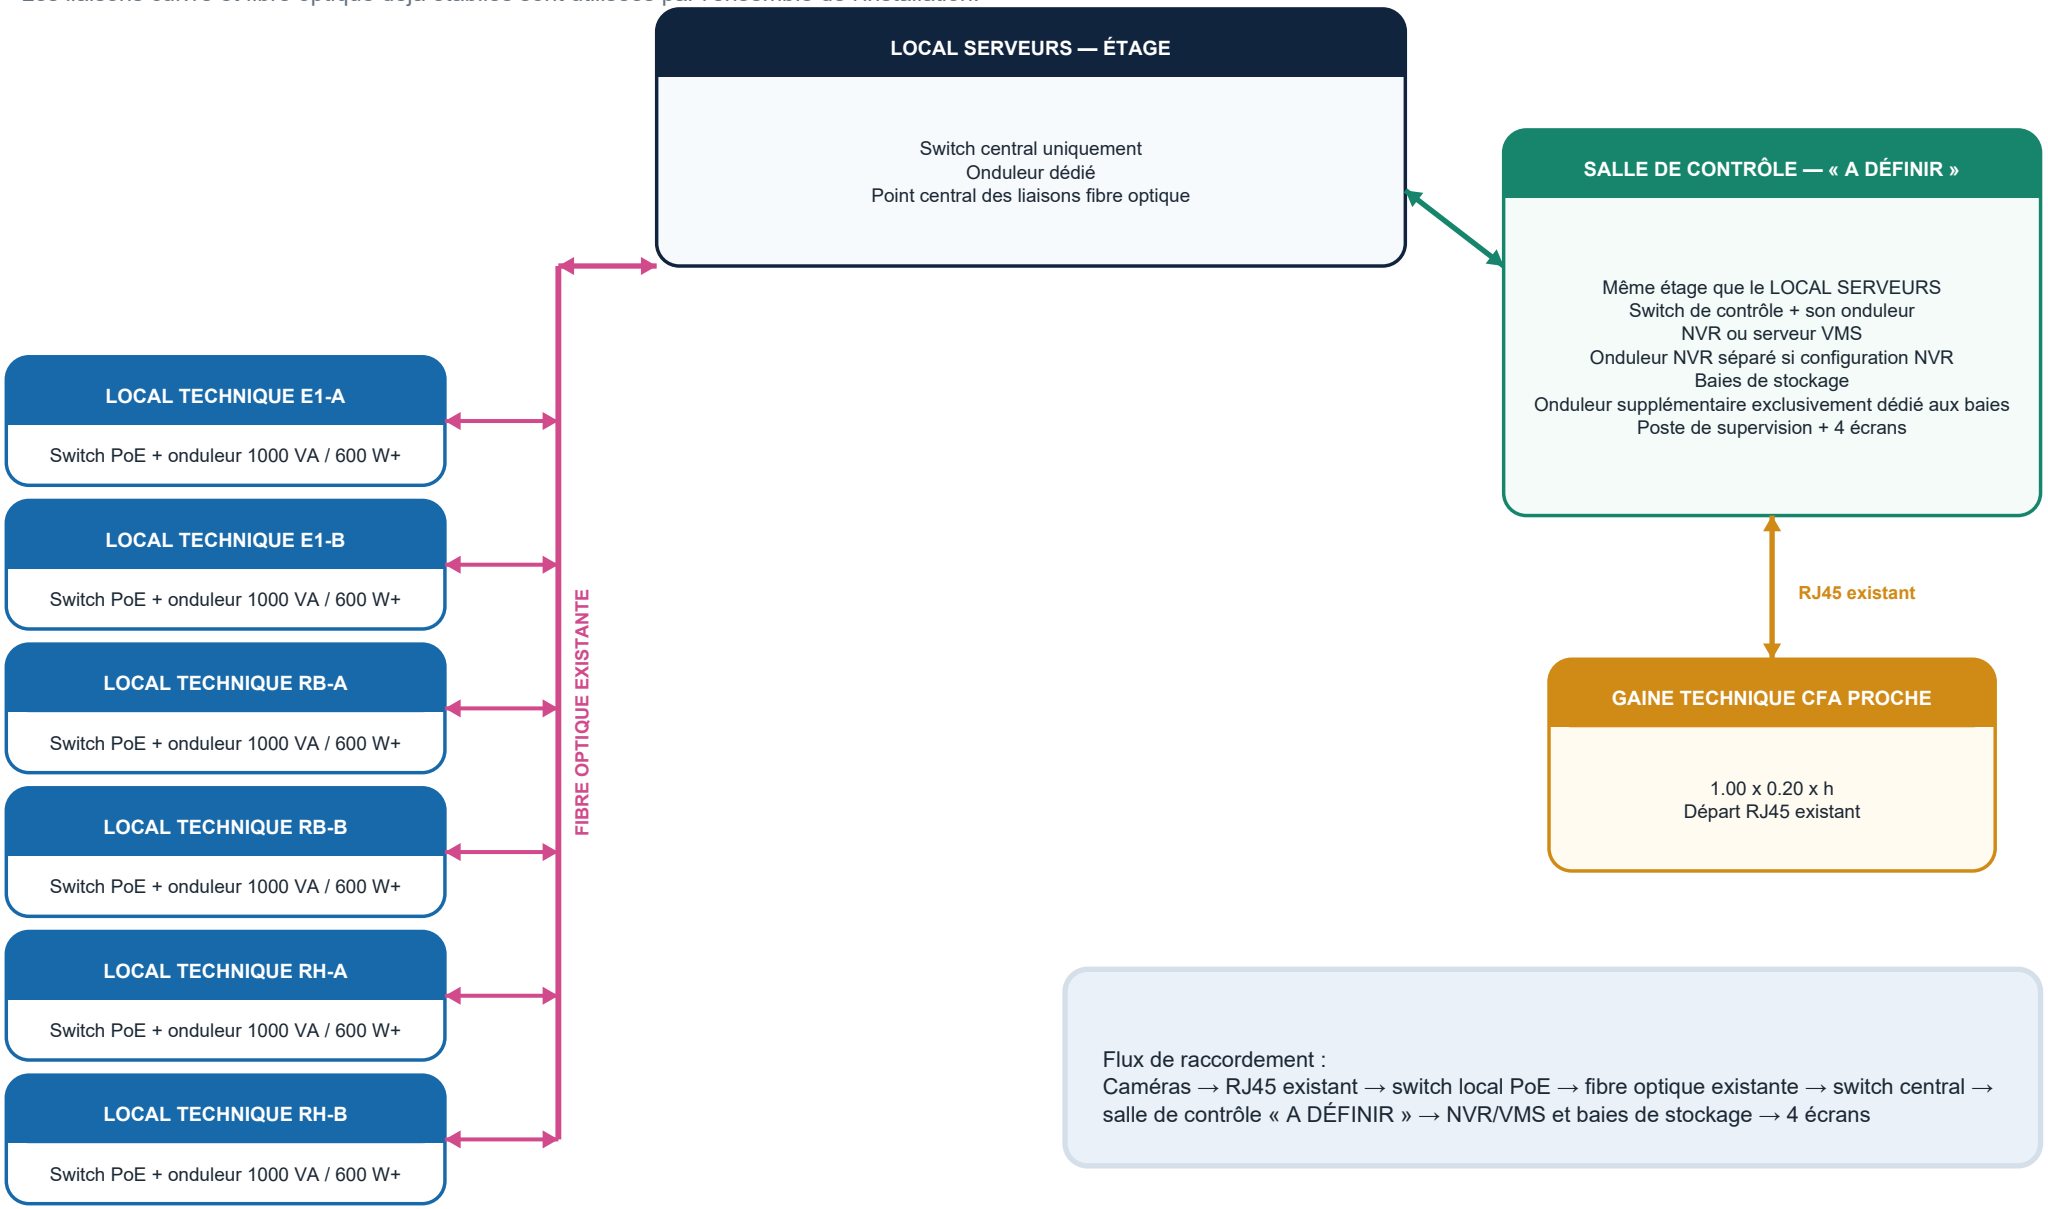

Flux de raccordement :
Caméras → RJ45 existant → switch local PoE → fibre optique existante → switch central → salle de contrôle « A DÉFINIR » → NVR/VMS et baies de stockage → 4 écrans

Implantation des équipements

Emplacement	Équipements installés	Raccordement dans l'architecture
Chaque local technique	1 switch local PoE 1 onduleur 1000 VA / 600 W+	Caméras par RJ45 existant Uplink par fibre optique existante vers le switch central
LOCAL SERVEURS — ÉTAGE	1 switch central uniquement 1 onduleur pour le switch central	Réunit toutes les fibres optiques provenant des locaux techniques et centralise le réseau
Salle de contrôle « A DÉFINIR » — ÉTAGE	1 switch de contrôle + son onduleur 1 NVR ou serveur VMS 1 onduleur NVR séparé si configuration NVR Baies de stockage 1 onduleur supplémentaire exclusivement dédié aux baies de stockage 1 poste de supervision + 4 écrans	RJ45 existant depuis la gaine technique CFA proche Connexion au même réseau de vidéosurveillance

Organisation par niveau

Niveau	Points techniques	Chemin réseau
ÉTAGE	Deux locaux techniques + LOCAL SERVEURS + salle de contrôle « A DÉFINIR »	Switchs locaux → fibre existante → switch central Gaine CFA proche → RJ45 existant → switch de contrôle → NVR/VMS et stockage
RDC BAS	Deux locaux techniques	Switchs locaux → fibre optique existante → switch central au LOCAL SERVEURS
RDC HAUT	Deux locaux techniques	Switchs locaux → fibre optique existante → switch central au LOCAL SERVEURS

PRINCIPE D'ENSEMBLE

Total : 8 switchs (6 locaux + 1 central + 1 contrôle). Configuration NVR : 10 onduleurs (8 pour les switchs + 1 réservé au NVR + 1 supplémentaire exclusivement réservé aux baies de stockage). Configuration VMS seul : 9 onduleurs (8 pour les switchs + 1 exclusivement pour les baies). Aucun de ces onduleurs n'est partagé.