
Raccordement global sur l'infrastructure vidéosurveillance

Même infrastructure physique, séparation logique par VLAN CONTRÔLE D'ACCÈS.

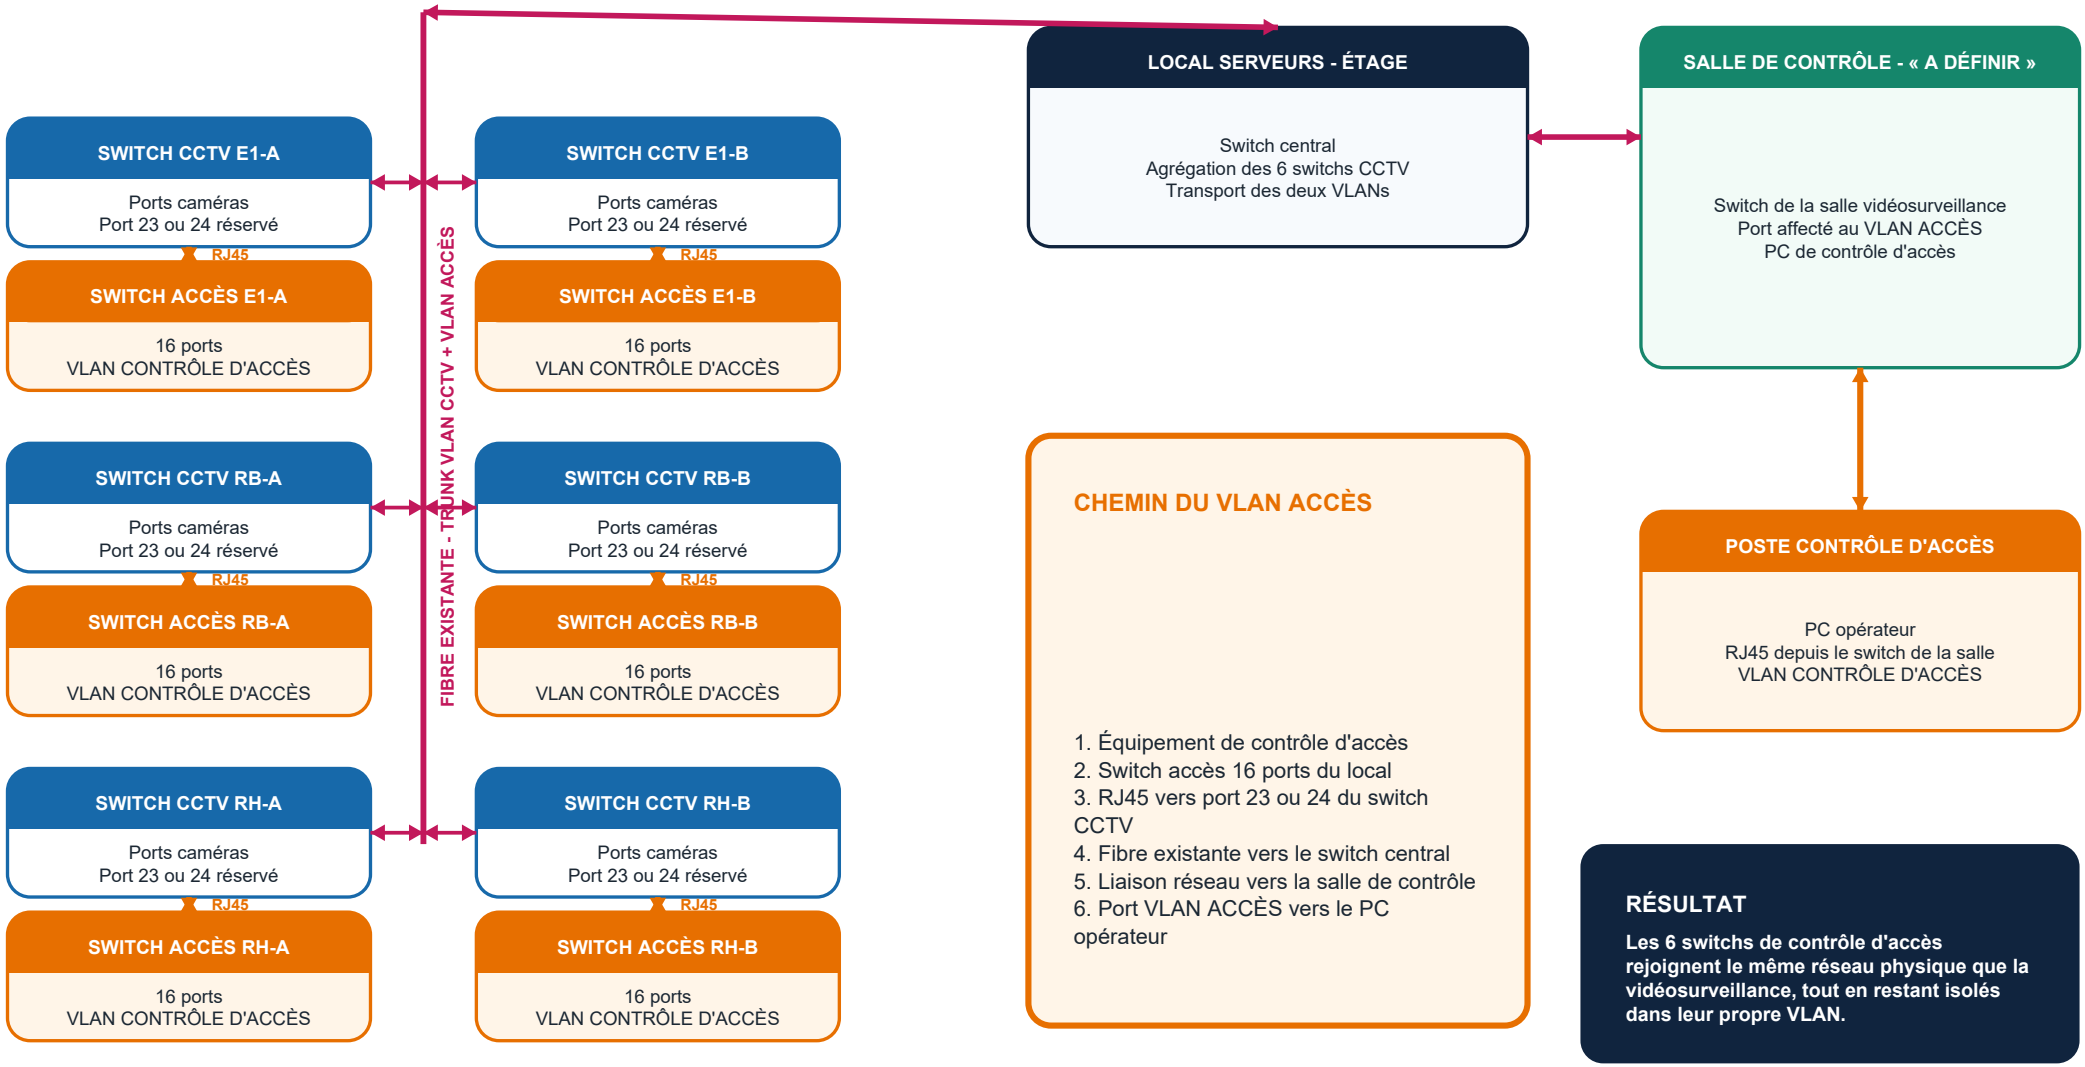

Affectation physique et logique

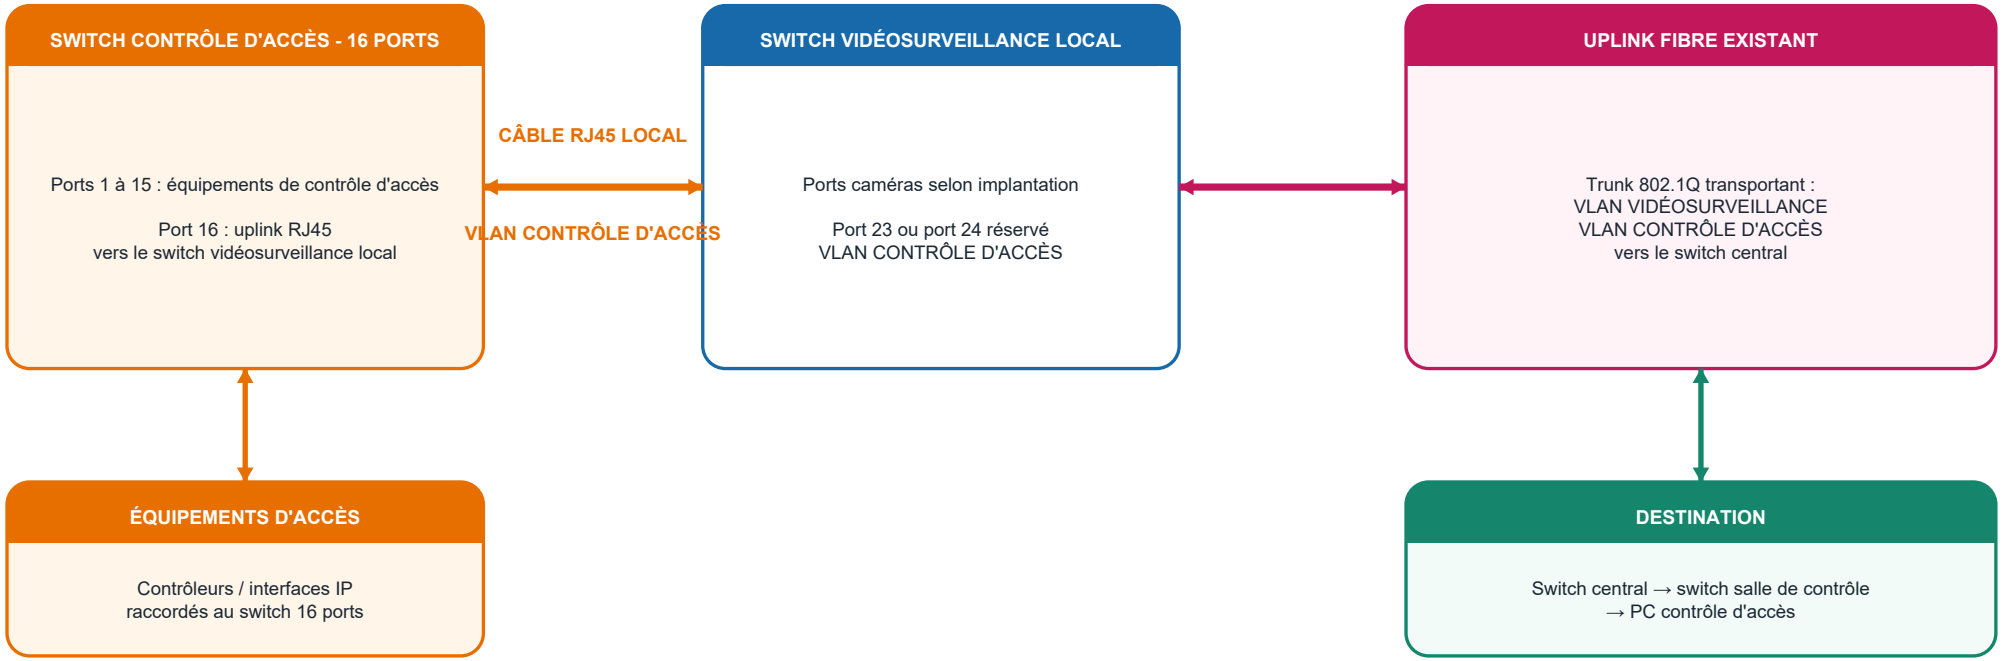


Table d'affectation

Équipement	Port	Affectation	VLAN / liaison
Switch contrôle d'accès 16 ports	1 à 15	Équipements de contrôle d'accès du local	VLAN CONTRÔLE D'ACCÈS
Switch contrôle d'accès 16 ports	16	Uplink RJ45 vers switch CCTV local	VLAN CONTRÔLE D'ACCÈS
Switch CCTV local	23 ou 24	Port réservé au switch de contrôle d'accès	VLAN CONTRÔLE D'ACCÈS
Switch CCTV local	Uplink fibre	Vers switch central du LOCAL SERVEURS	Trunk : VLAN CCTV + VLAN ACCÈS
Switch salle de contrôle	Port PC	PC de contrôle d'accès	Port d'accès dans le VLAN CONTRÔLE D'ACCÈS